


Planta base do térreo

V08 / Revisão 05 • Ajustes conforme marcações • Térreo e lazer • Casa de aproximadamente 370 m²

RUA LATERAL • ESQUINA

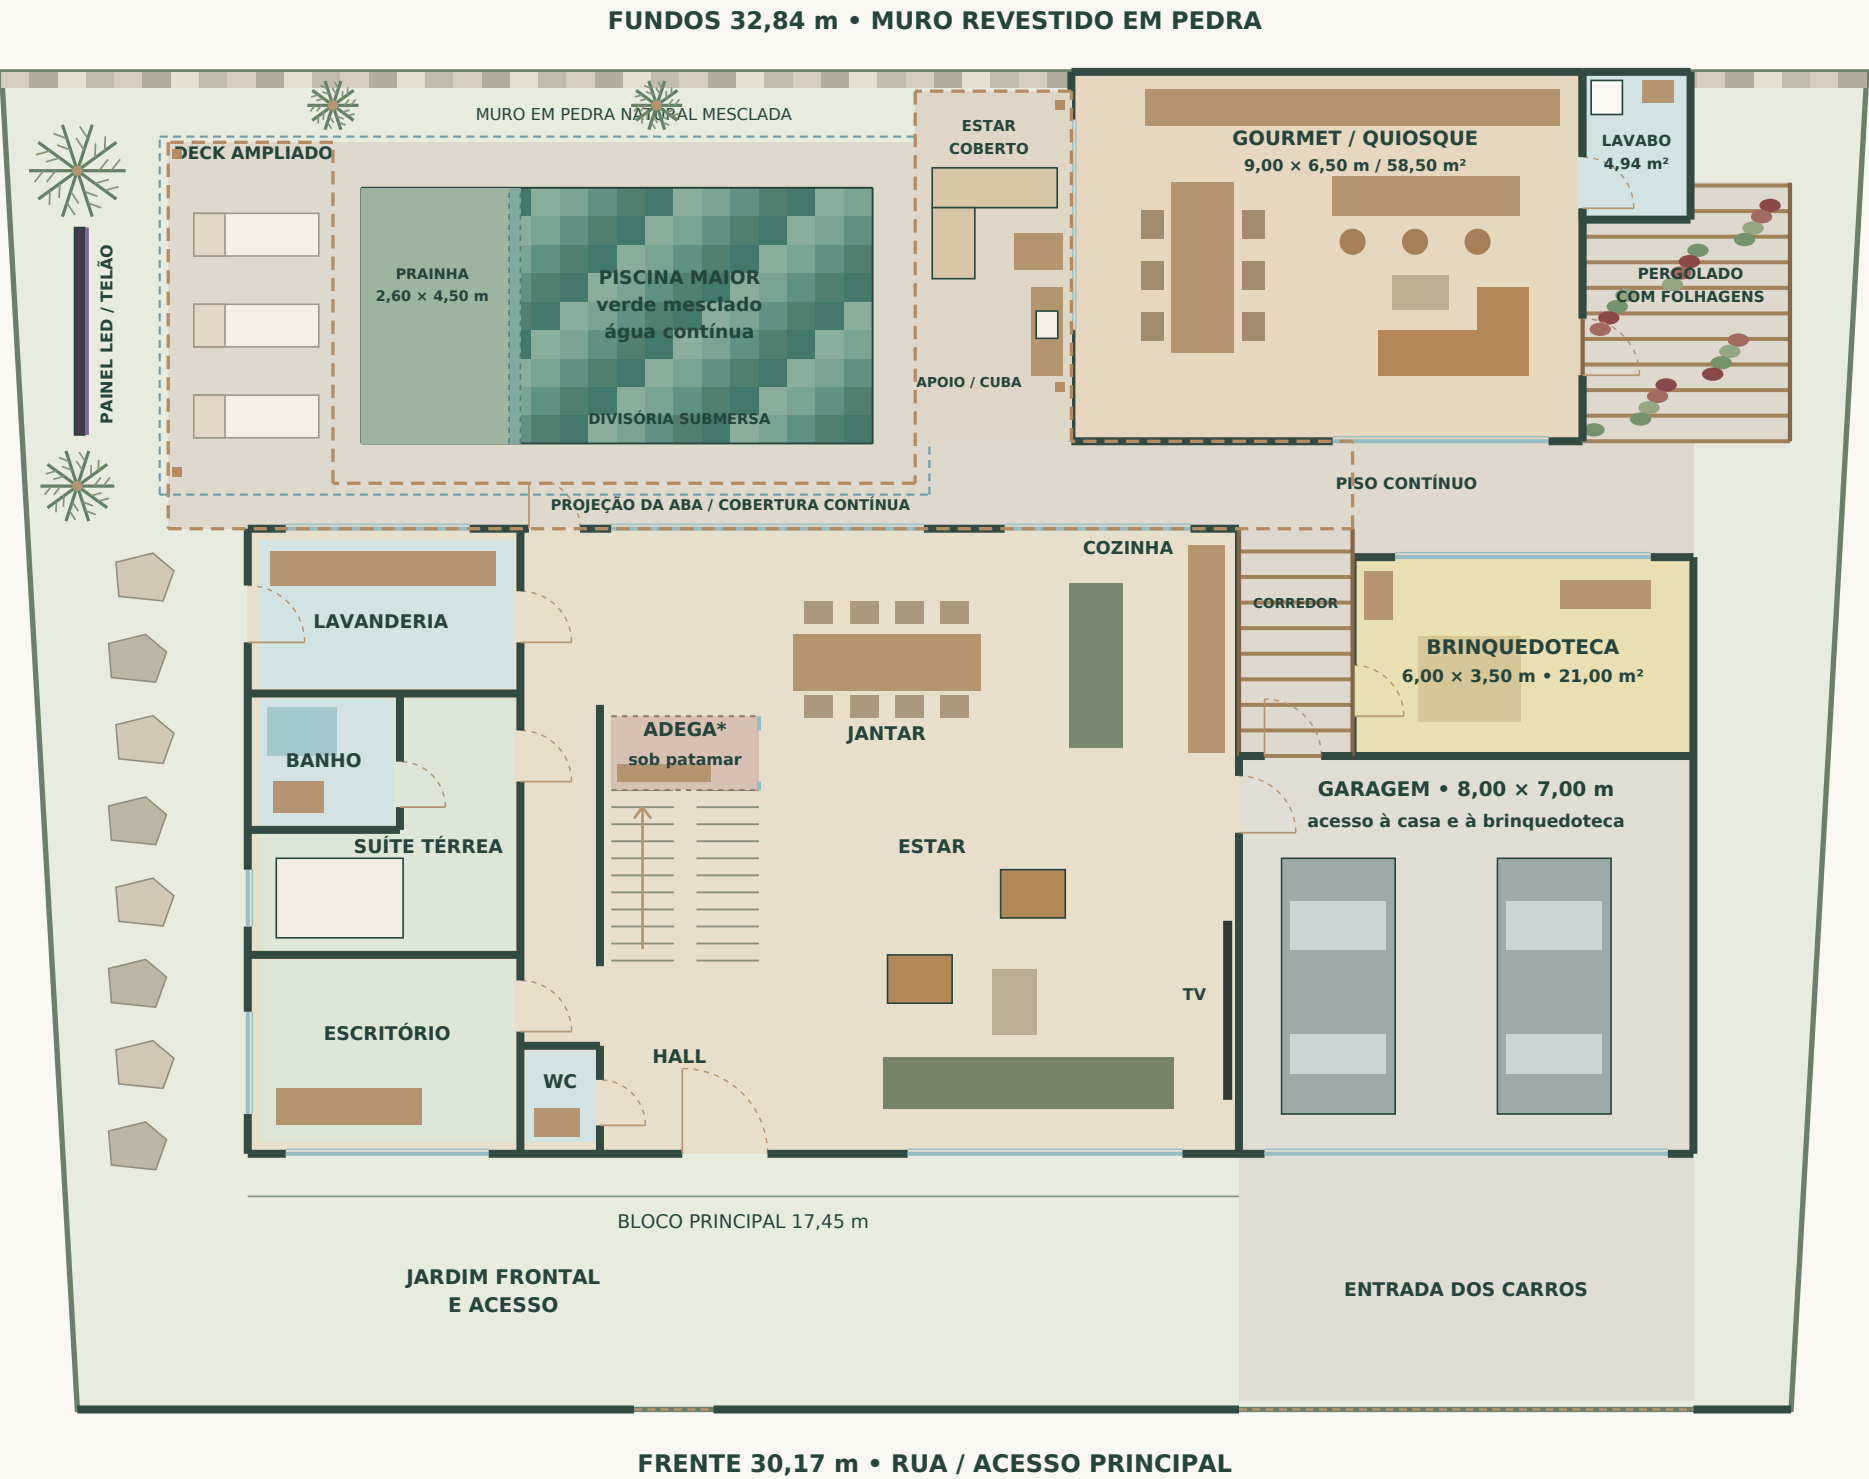

01 / QUIOSQUE AMPLIADO

Parede esquerda avançada 1,00 m conforme a marcação. Área fechada passa de 52,00 para 58,50 m², com 9,00 x 6,50 m. Mesa e cadeiras mantidas na posição, ganhando circulação no lado esquerdo.

02 / LAVABO COM MAIS ESPAÇO

Parede frontal avançada 0,65 m. Lavabo passa a 1,90 x 2,60 m, com 4,94 m². Porta de 0,90 m deslocada para a frente, abrindo para dentro; cuba e vaso ficam na parte posterior.

03 / INTEGRAÇÃO EXTERNA

A ampliação aproveita parte do estar coberto. Banco e apoio externo ajustados junto à nova parede; piso contínuo preservado. O lavabo ocupa parte do pergolado existente, sem crescer para fora do terreno.

04 / ÁREAS PRESERVADAS

Casa permanece com 370,10 m² nos dois pavimentos. Mantidos piscina, telão, palmeiras, garagem, brinquedoteca e demais ambientes. Quadro atualizado para separar áreas fechadas e coberturas abertas.

ÁREAS DO ESTUDO

Casa / térreo	191,95 m²
Casa / superior previsto	178,15 m²
CASA / DOIS PAVIMENTOS	370,10 m²
Varanda / reserva	31,41 m²
Garagem ampliada	56,00 m²
Brinquedoteca fechada	21,00 m²
Quiosque + lavabo ampliados	63,44 m²
Pergolado / projeção	23,37 m²
Aba externa / projeção	56,71 m²
SOMA DAS ÁREAS DO ESTUDO	622,03 m²
Piscina / fora do total	40,50 m²

Soma inclui projeções das coberturas. Pisos descobertos, piscina e jardins ficam fora. Estudo conceitual, sem cálculo legal de área construída.

AZUL: VIDRO • TRACEJADO CAMELO: ABA DE COBERTURA • RIPAS: PERGOLADO • BEGE EXTERNO: PISO

* Adega: posição sob o patamar reservada conforme marcação; acesso em pé depende de redesenhar a escada em corte.

Aba com laterais abertas: projeção e apoios preliminares; estrutura, drenagem e recuos a dimensionar. Piscina: níveis a definir em corte.

Perímetro equivalente, sem levantamento das curvas. Superior e varanda permanecem como reservas de área; não foram redesenhados.